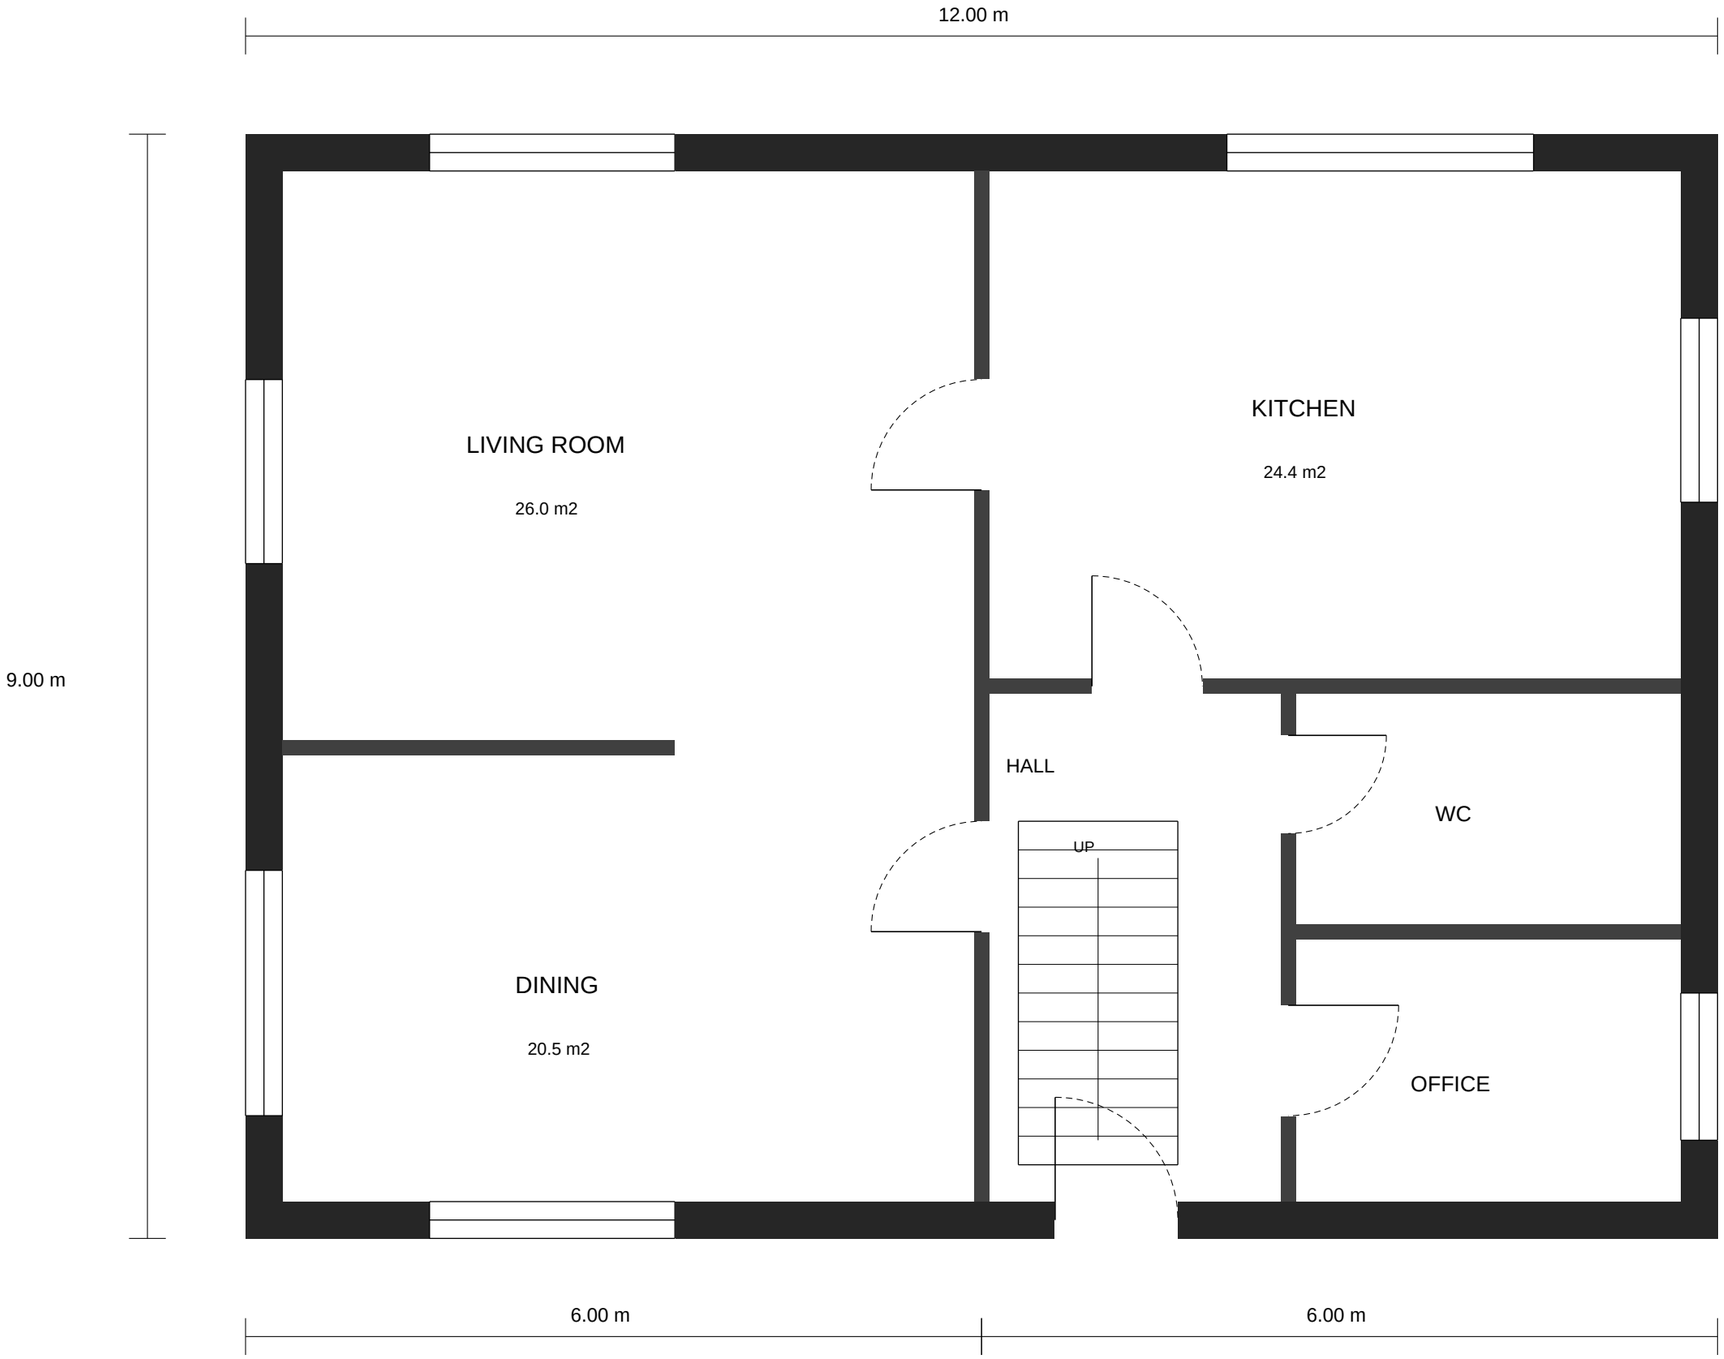

SAMPLE HOUSE

Ground floor plan

Scale 1:50 at A3

Overall 12.00 m x 9.00 m

Sheet 1 of 2

Test drawing for Electro House.
Not a real building. Calibrate on the
12.00 m dimension or use paper scale 1:50.

0 1 5 m

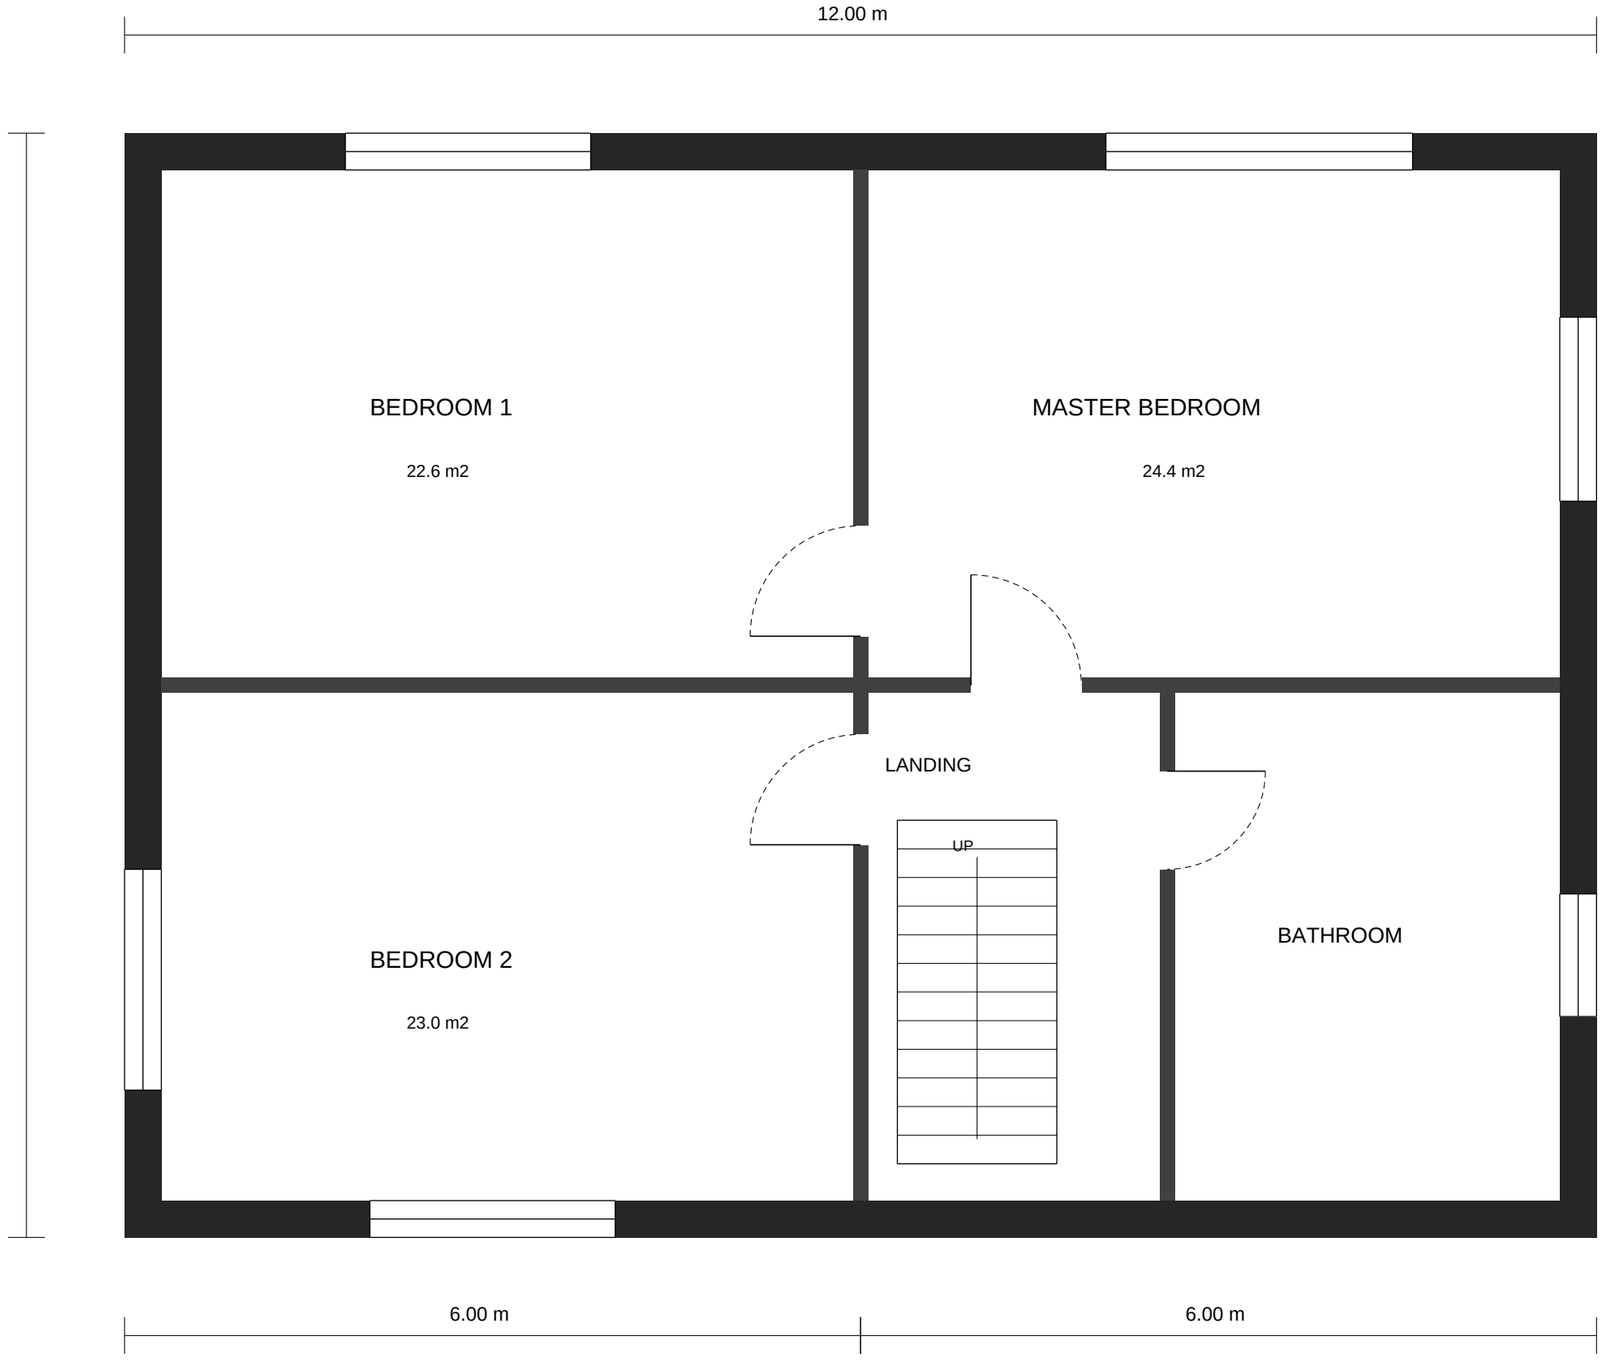

SAMPLE HOUSE

First floor plan

Scale 1:50 at A3

Overall 12.00 m x 9.00 m

Sheet 2 of 2

Test drawing for Electro House.
Not a real building. Calibrate on the
12.00 m dimension or use paper scale 1:50.

0 1 5 m